


Plano conjunto del soportal

Plantas bajas de los seis bloques · delimitación interpretativa y elementos originales

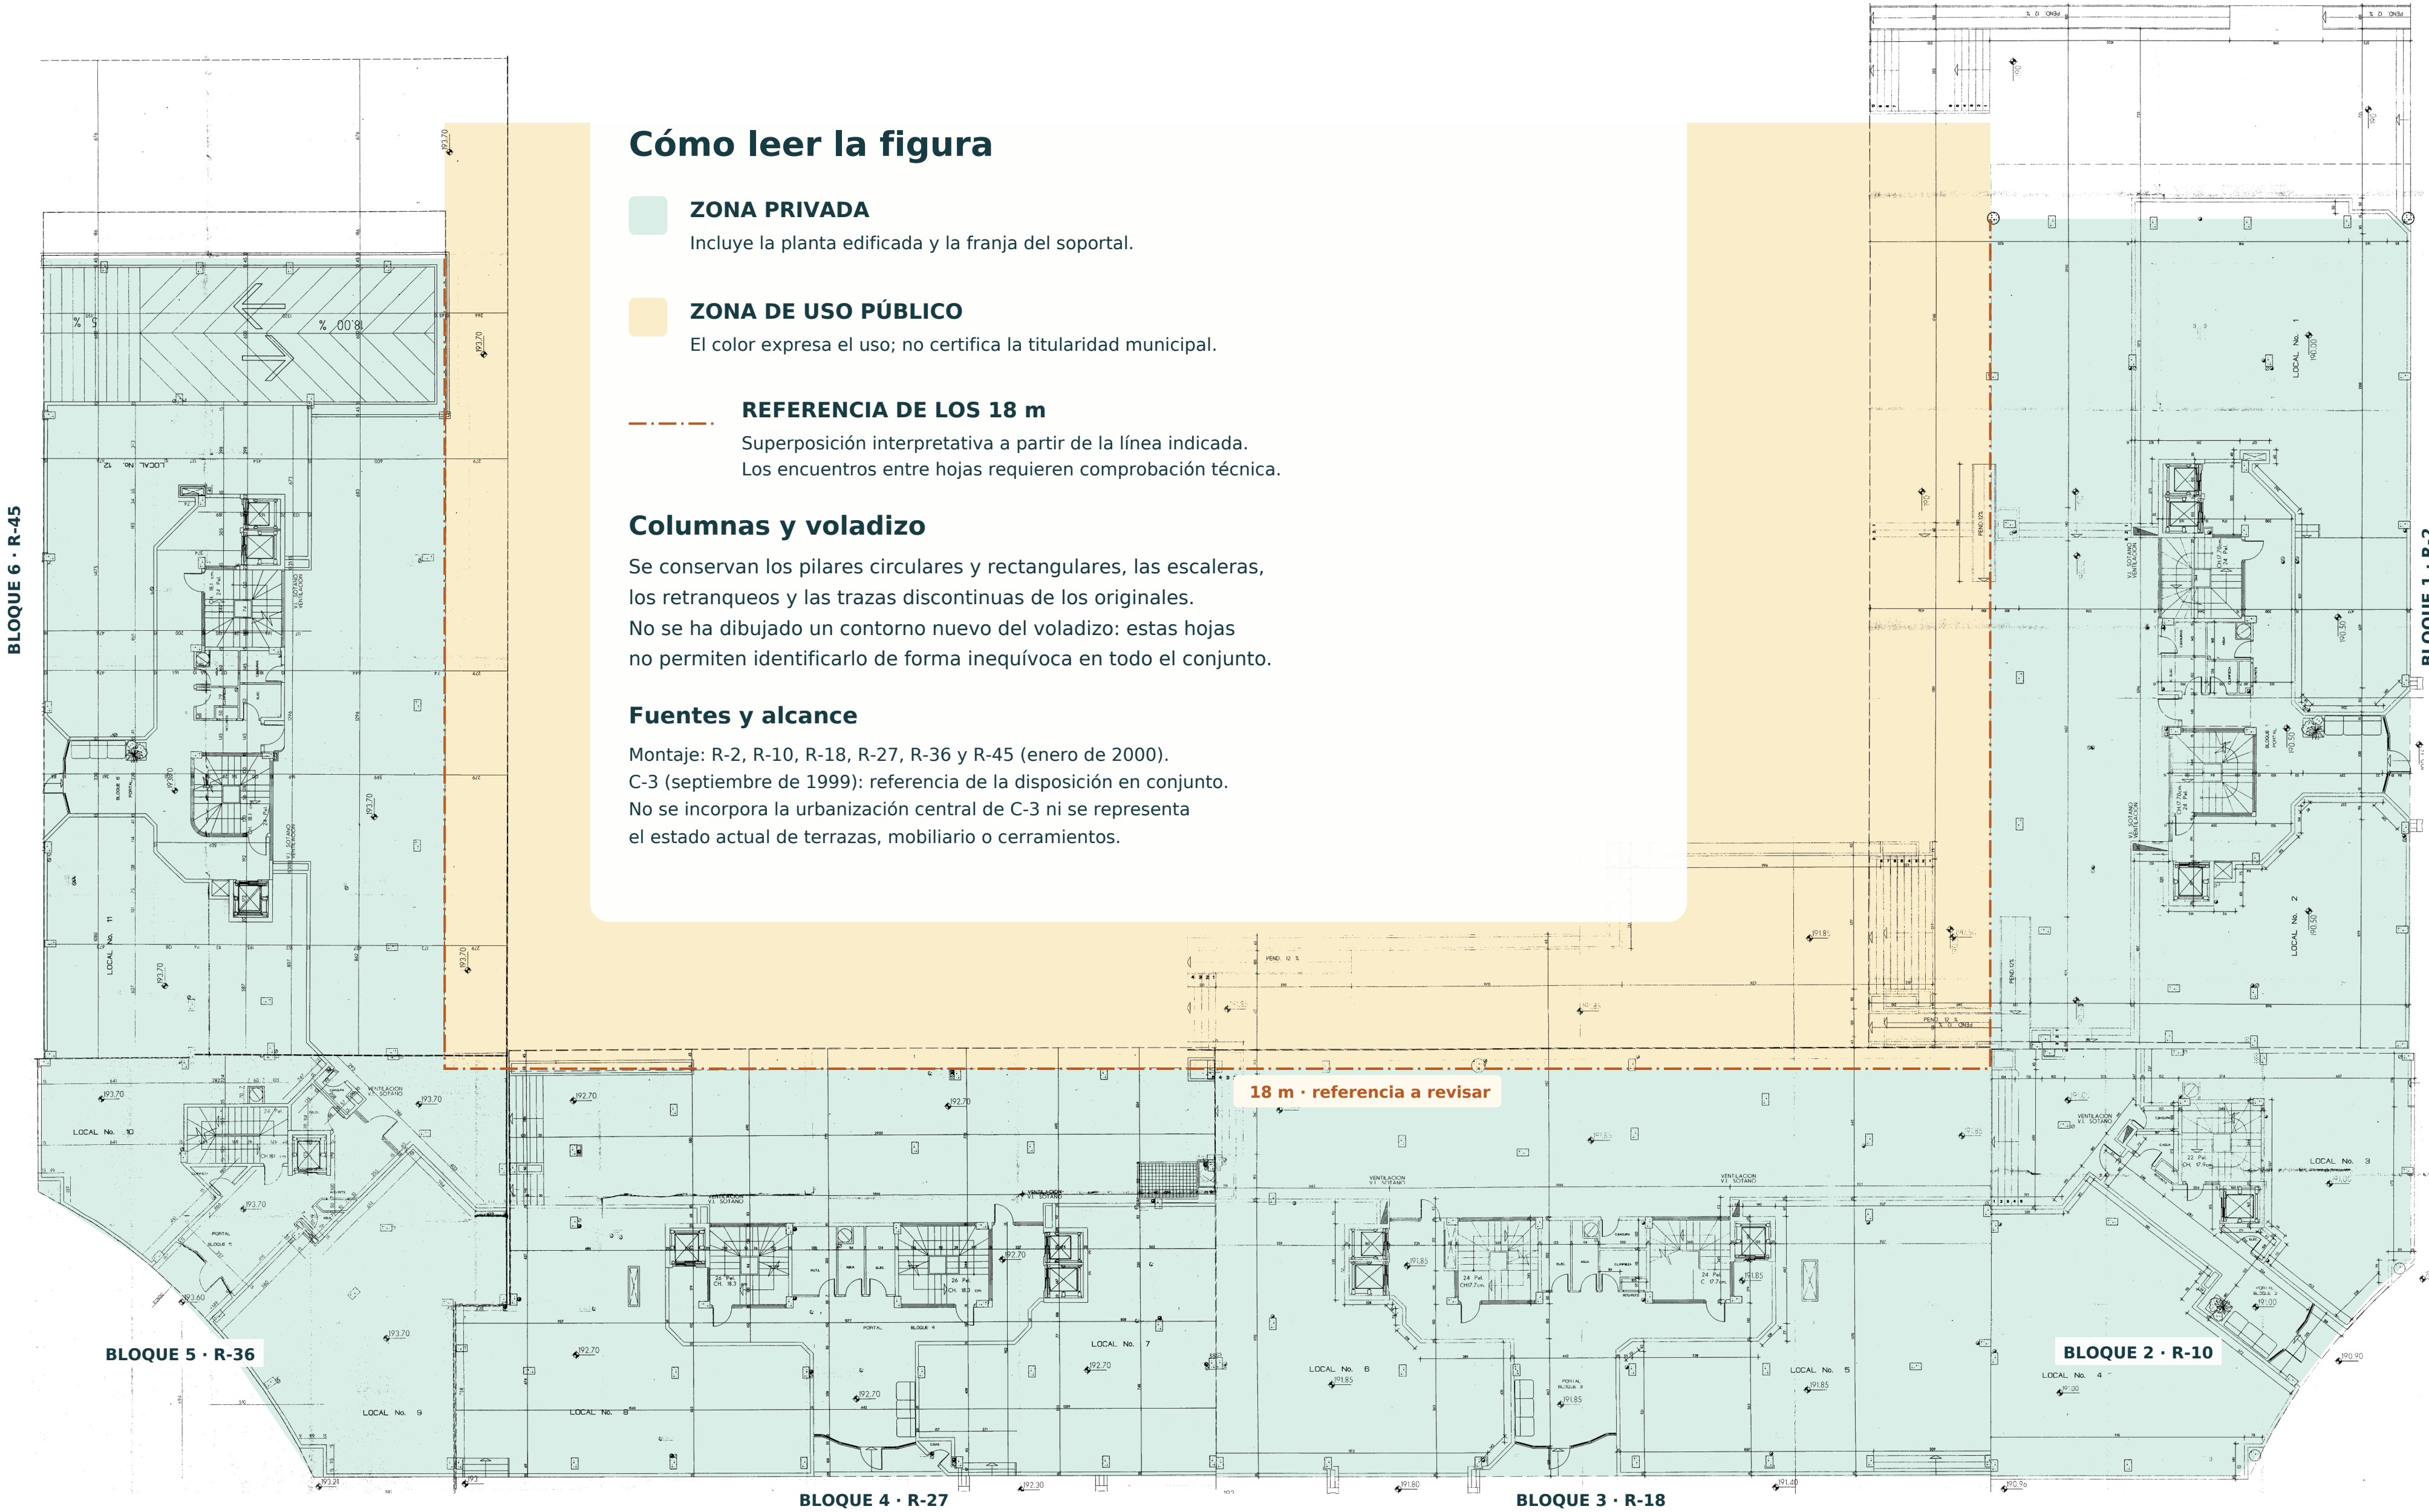

Criterio de uso: Informe jurídico de 16.07.2026, p. 11, que diferencia uso privado comunitario y uso público.
Para una versión definitiva: comprobar el trazado de los 18 m y el voladizo con el plano acotado correspondiente y el técnico.